


FULL-FLOOR RESIDENCE

TWO MIRRORED 2-BHK UNITS MERGED INTO ONE HOME · PROPOSED FURNITURE LAYOUT PLAN

DIMENSIONS IN MILLIMETRES AND FEET-INCHES · CEILING 3050 (10'-0") THROUGHOUT; TERRACES UNDER A HIGH-LEVEL GLASS ROOF · CONCEPT DRAWING, NOT FOR CONSTRUCTION

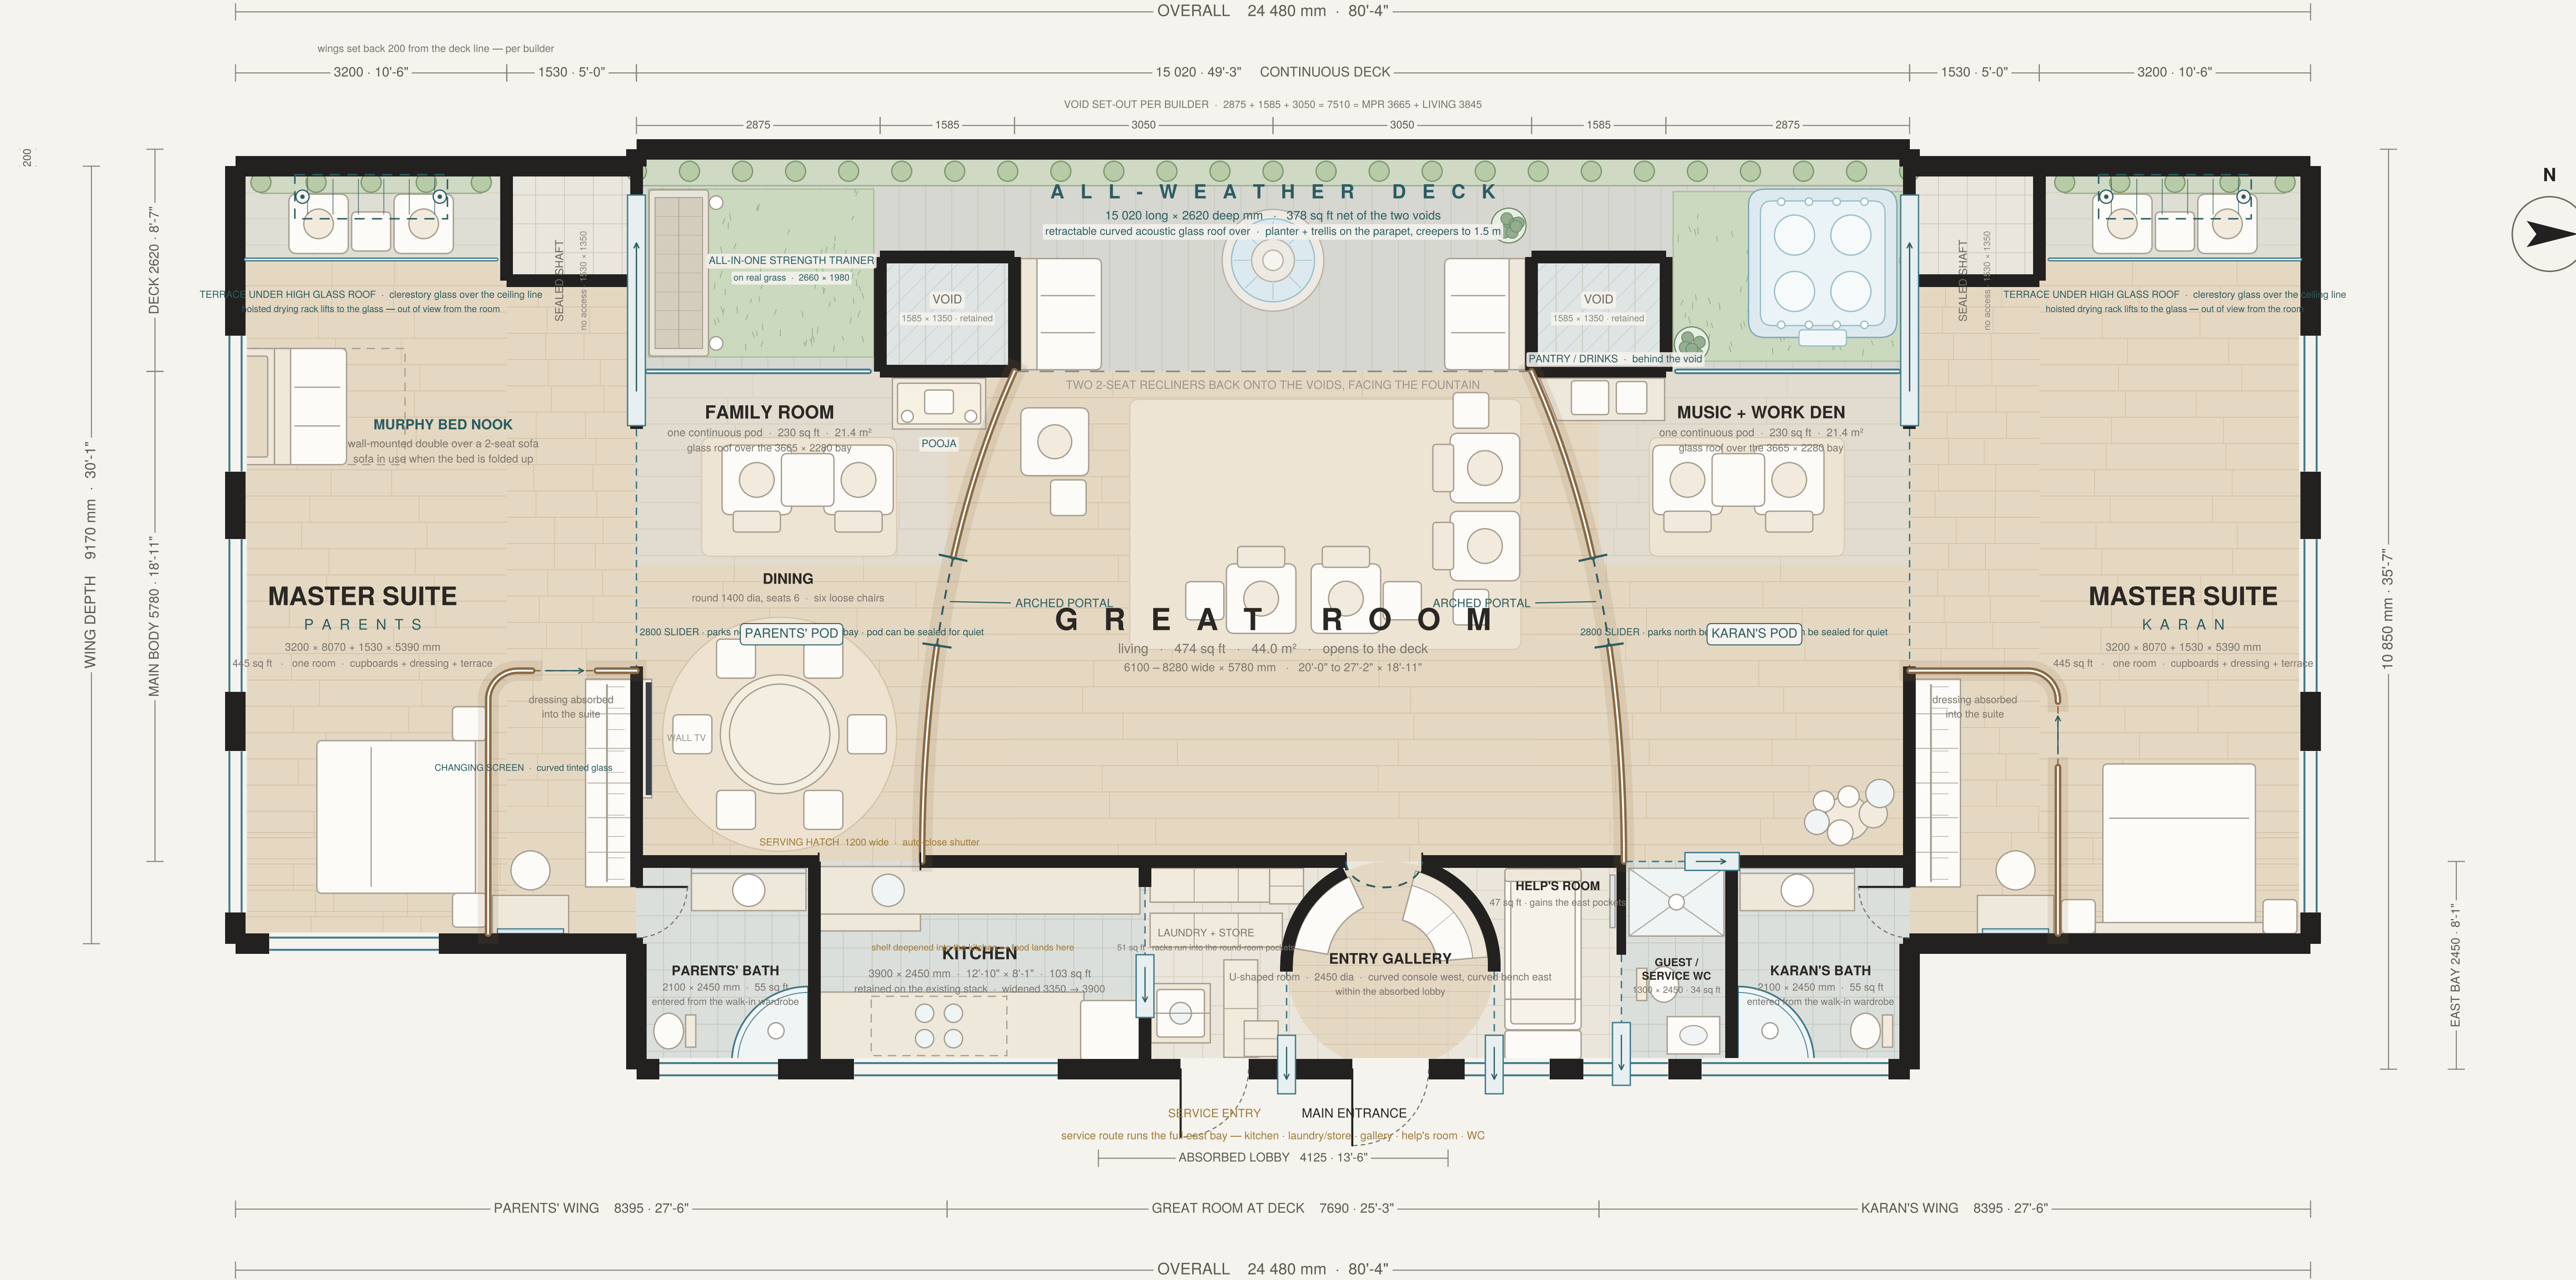

MASONRY TINTED CURVED GLASS GLAZING GLASS ROOF OVER SEALED SERVICE ZONE BUILDING CORE / VOID ARCHED OPENING

FULL-FLOOR RESIDENCE	DWG A-101 · REV 101	
PROPOSED FURNITURE LAYOUT PLAN	SCALE 1:75 @ A1	DRAFT FOR
GROSS 2 688 SQ FT (249.7 m²) — RECONCILED EXACTLY	AUGUST 2026	INTERIOR
TWO FLATS 2 579 SQ FT + ABSORBED LOBBY 109 SQ FT	ISSUE: CONCEPT	DESIGNER