


OM NEELDHARA — FLOOR 14 · HOME 1

Every space and every significant piece: length × width × height, in feet and inches

scale 1:35 on A1

Round 1 layout · concept drawing, not for construction

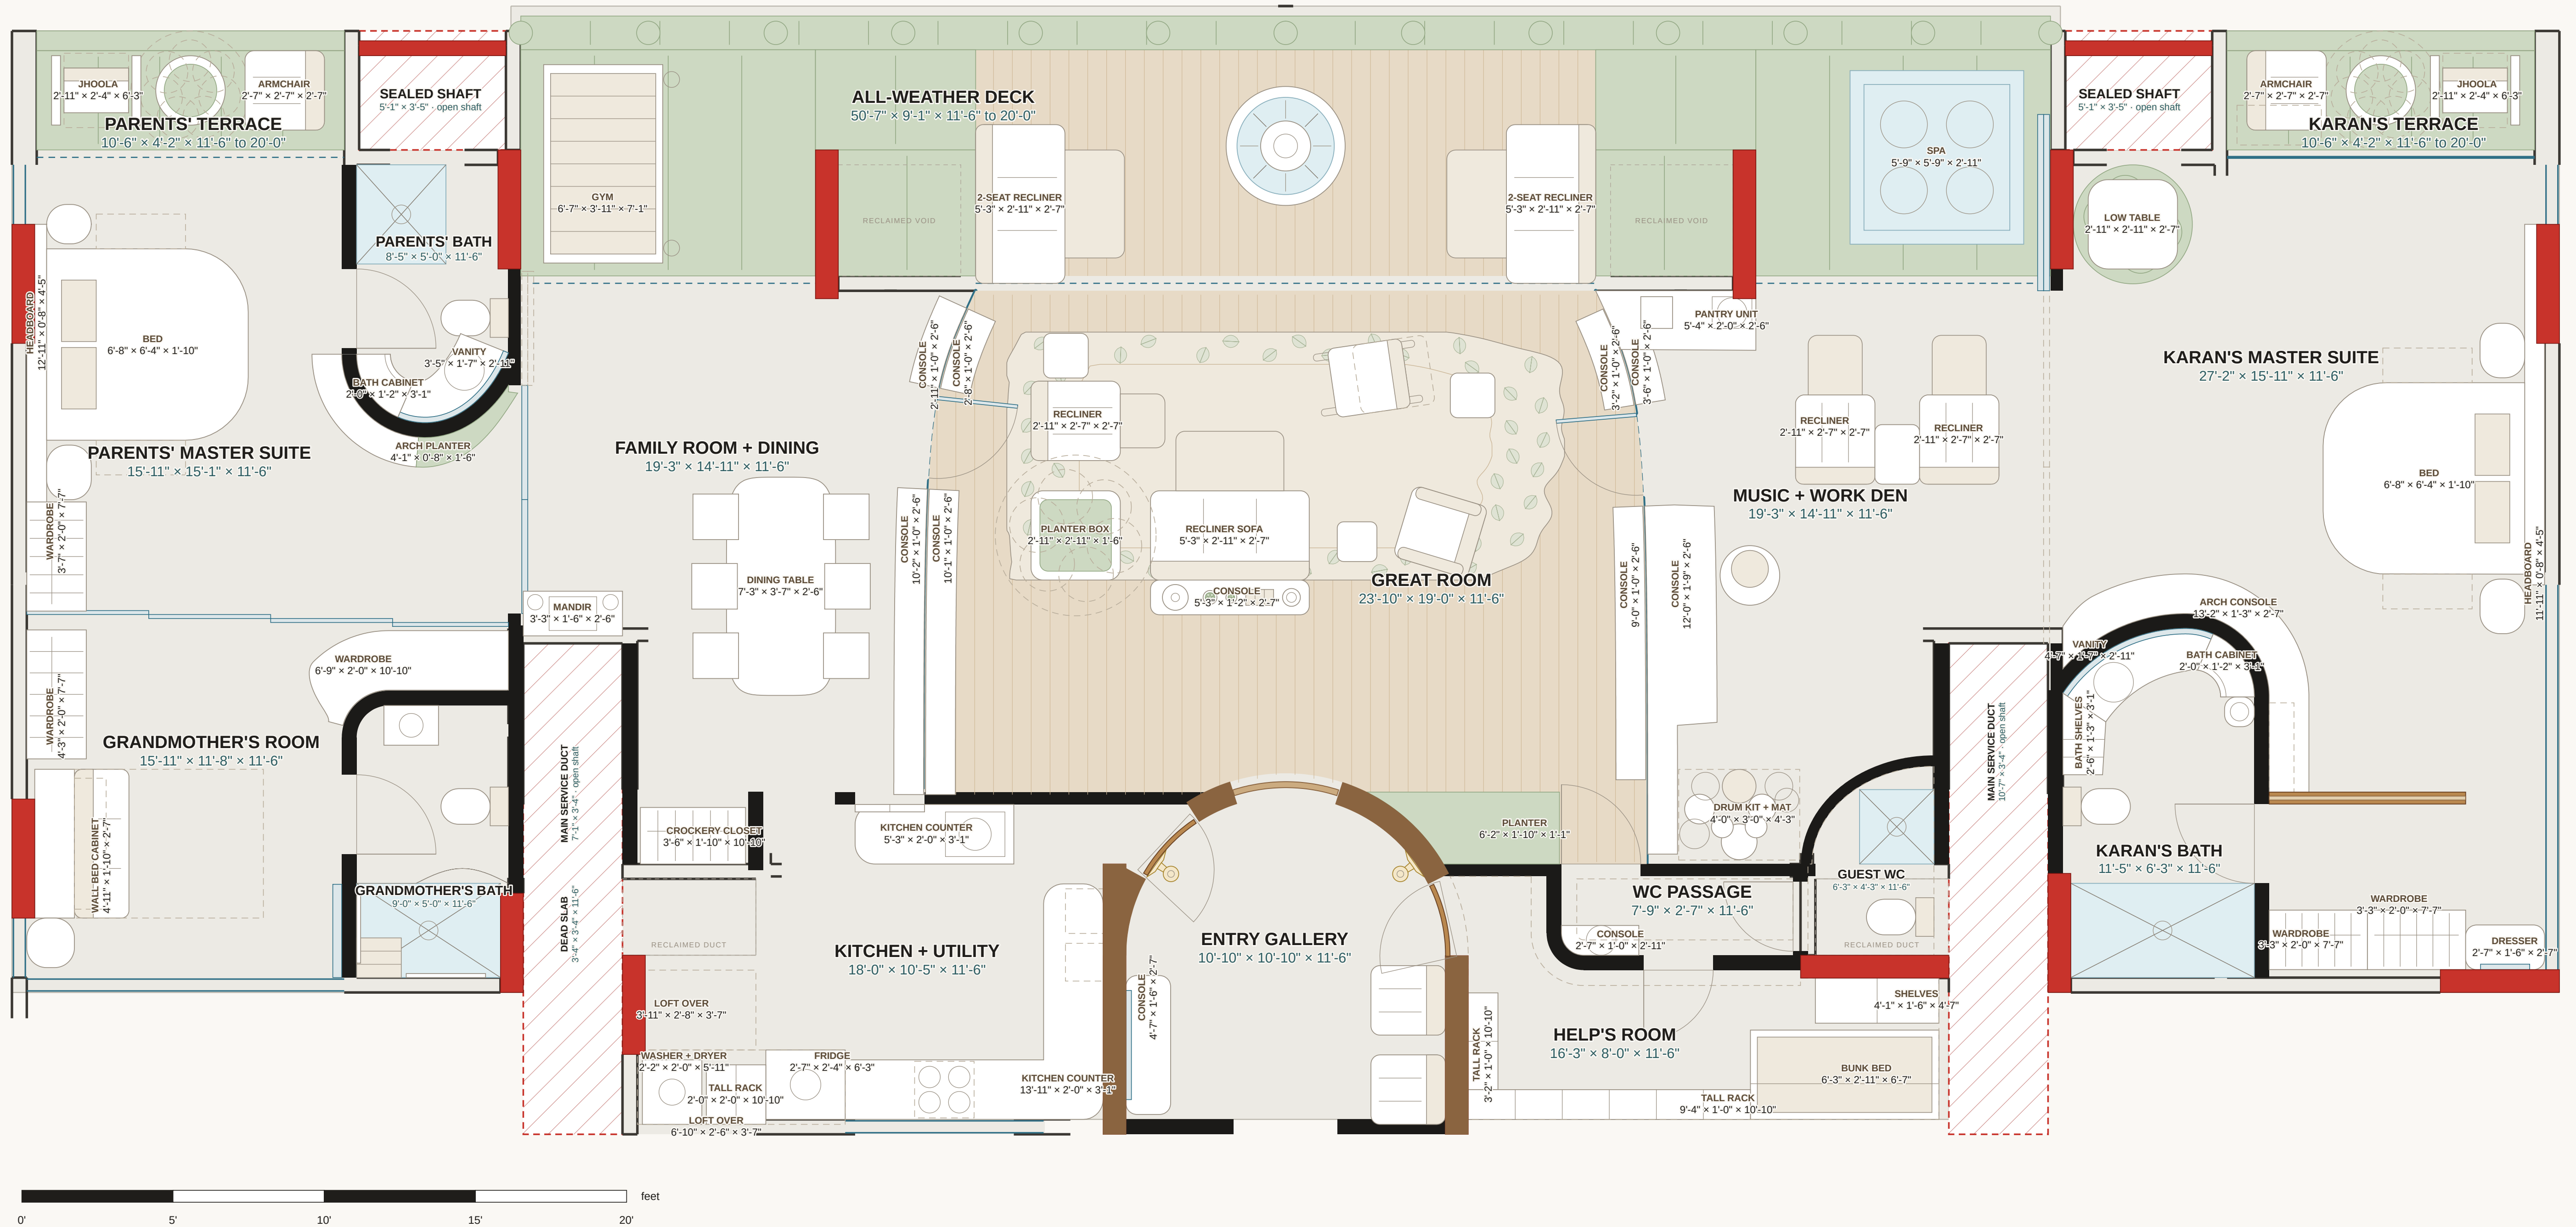

Spaces: length x width are the overall extent of the space, longest side first; height is floor to ceiling. The deck and the two terraces are open to the glass vault, which rises from the ceiling line to its crown. Shafts and ducts are open through the building and carry no ceiling height.

Furniture and joinery: length $\times$ width $\times$ height of the piece. A curved or L-shaped run is measured along its length, at its working depth. A loft is sized by its box and hangs above what is drawn under it.